



CONCEPT, NOT FOR FABRICATION

GrainGuard · github.com/BoujeeEnjinia1701/grainguard

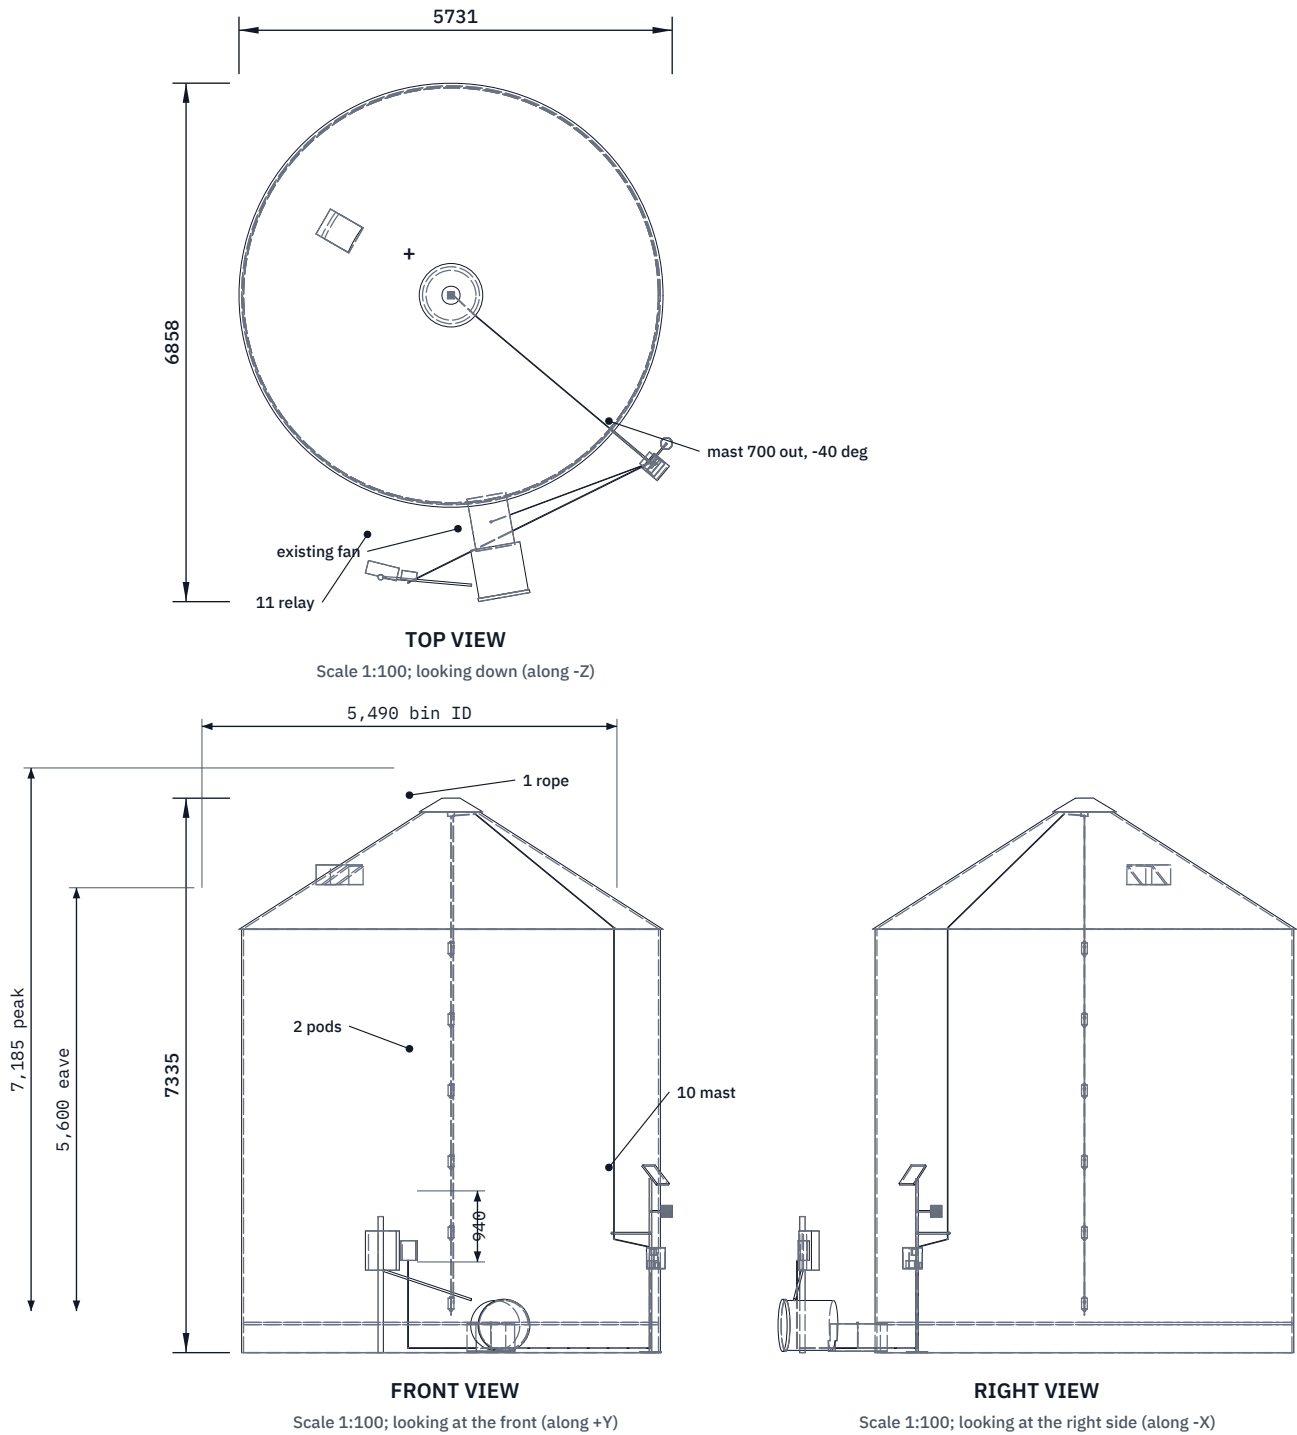


REV	DESCRIPTION	DATE	BY
P1	Preliminary GA for TRL 3 (from cad/src/model.py)	2026-09-25	AC
P2	Plenum probe in base kit; kit cost note (GGD-DDR-002)	2026-09-25	AC
P3	Solar panel faces away from the bin (GGD-DDR-002)	2026-09-27	AC
P4	Layout and labels tidied	2026-09-27	AC

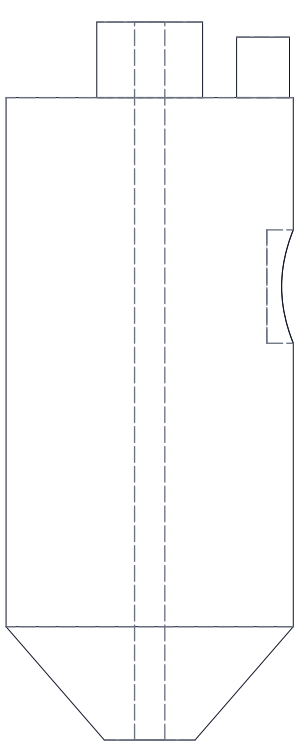

DETAIL A: SENSOR POD

Scale 1:2

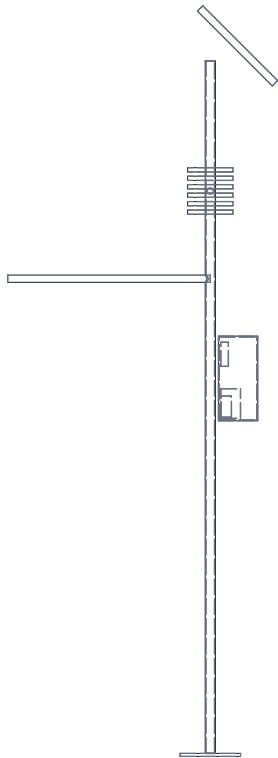

DETAIL B: MAST AND CONTROLLER

Scale 1:25, radial view

MAIN DIMENSIONS AND INTERFACES (MM)

Reference bin 5,490 ID, eave 5,600, floor +400; grain 5,200 deep
Rope 6 from rated center hanger at 7,125; hung length 6,625
Pods 76 dia x 140; 6 at 940 pitch, 250 above floor
Bus cable route 14.6 m via peak cap; 16 m supplied
Mast DN25 x 2,300, 700 outside wall; stay at 1,580
Enclosure 280 x 230 x 130 IP66 at 1,250; panel 10 W at 45 deg
Relay kit at existing starter; 14 plenum probe in fan transition
Design pull-down 2.5 kN (GGD-CAL-001); kit \$256.50 per bin

GRAINGUARD

github.com/BoujeeEnjinia1701/grainguard

General arrangement

DRAWING NO. GGD-DWG-001		REV P4	SHEET 1 of 1	SIZE ANSI B
SCALE 1:100	UNITS mm	PROJECTION 	DATE 2026-09-27	DRAWN Amish Chadha
MATERIAL / NOTES Bin, floor, fan and starter existing (reference only); kit parts per bom/bom.csv. PRELIMINARY, NOT FOR FABRICATION				
Licensed CERN-OHL-S-2.0 · Design Molecule Lab · designmolecule.com			Generated from cad/src; do not edit by hand	